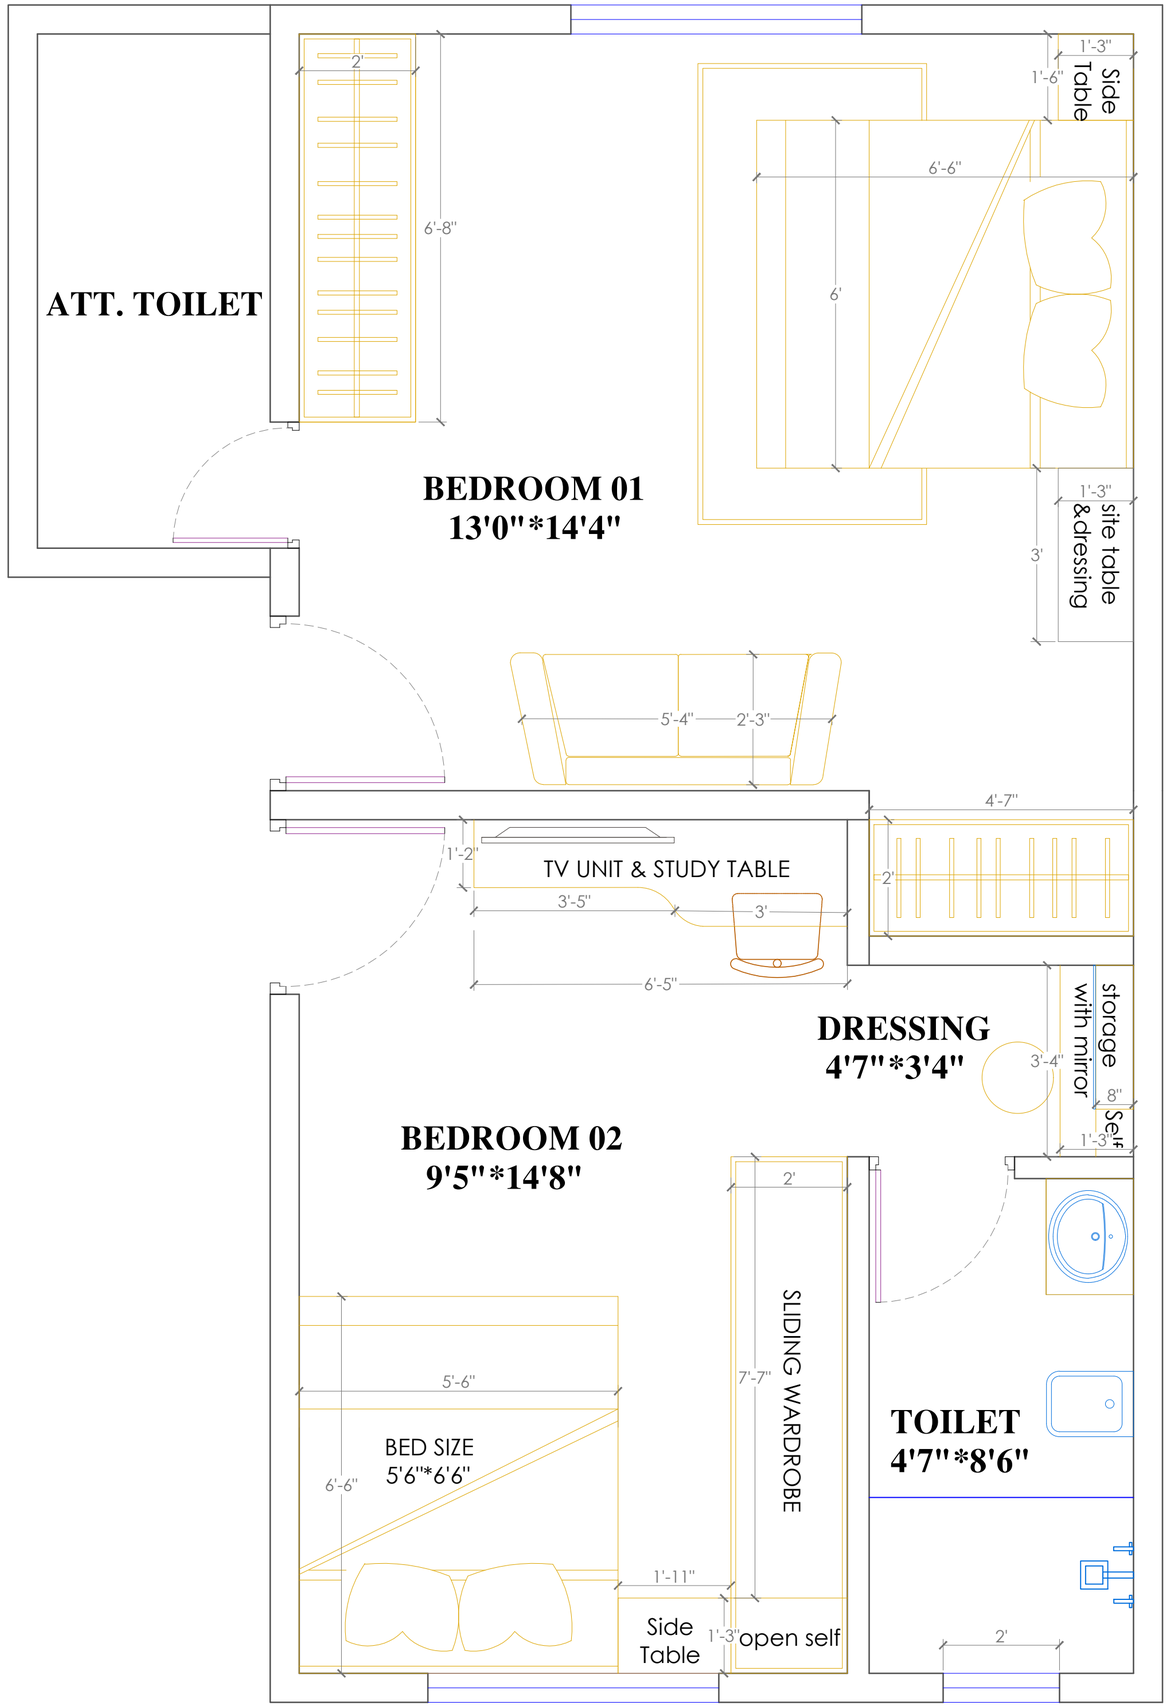
ATT. TOILET
2'
6'-8"
BEDROOM 01
13'0"*14'4"
1'-3"
1'-6"
Side Table
6'-6"
6'
1'-3"
site table &dressing
3'
5'-4"
2'-3"
4'-7"
1'-2"
TV UNIT & STUDY TABLE
3'-5"
3'
6'-5"
2'
DRESSING
4'7"*3'4"
3'-4"
storage with mirror
8"
Self
1'-3"
BEDROOM 02
9'5"*14'8"
2'
SLIDING WARDROBE
7'-7"
5'-6"
BED SIZE
5'6"*6'6"
6'-6"
TOILET
4'7"*8'6"
1'-11"
Side Table
1'-3"
open self
2'